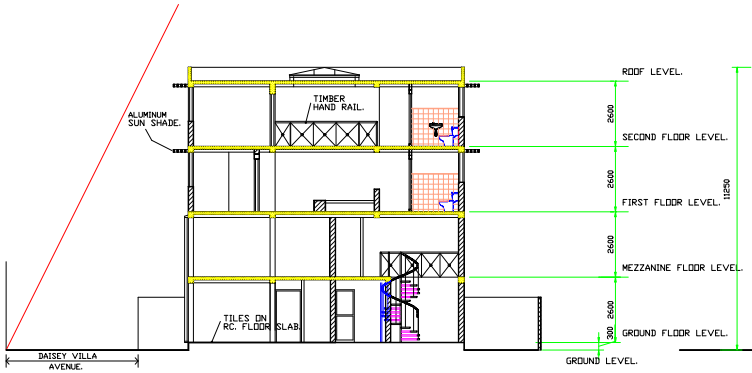


SECTION A:A

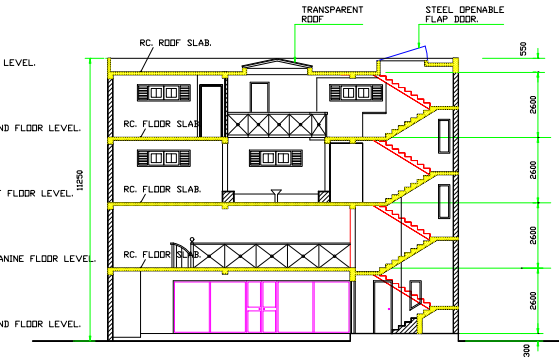


SECTION B:B

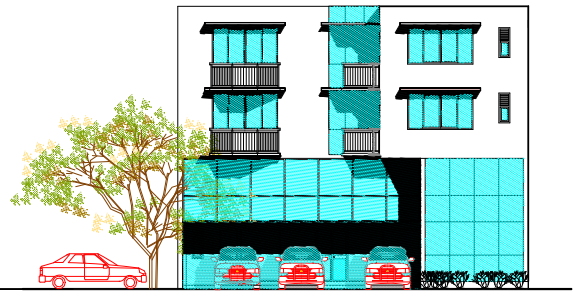

FRONT ELEVATION

## SCHEDULE OF DOORS AND WINDOWS

| TYPE | SIZE | DESCRIPTIONS | Nos. | Type | SIZE | DESCRIPTION | Nos. |
|---|---|---|---|---|---|---|---|
| D1 | 1500x2100 | ALUMINUM GLAZED SLIDING DOOR | 01 | W1 | 3125+2870X2100 | ALUMINIUM GLAZED SHOP FRONT WINDOW | 01 |
| D2 | 1150x2100 | ALUMINUM GLAZED SIDE HUNG DOOR | 01 | W2 | 1750+3900X2100 | -DO- | 01 |
| D3 | 750x2100 | TIMBER DOOR | 02 | W3 | 600X1500 | TIMBER WINDOW | 01 |
| D4 | 1000x2100 | ALUMINUM GLAZED DOOR | 01 | W4 | 9450X2100 | ALUMINIUM GLAZED SHOP FRONT WINDOW | 01 |
| D5 | 750x2100 | STD. TIMBER PLYWOOD DOOR (MARINE TYPE) | 07 | W5 | 3800+3100X2100 | -DO- | 01 |
| D6 | 900x2100 | TIMBER DOOR | 05 | W6 | 1100X1000 | ALUMINIUM | 07 |
| D7 | 1150x2100 | SOLID TIMBER PANELED DOOR | 01 | W7 | 3750X2300; 1500 | -DO- | 02 |
| D8 | 900x2100 | TIMBER PANELED DOOR (DOUBLE SASHES) | 02 | W8 | 2600X2300 | -DO- | 02 |
| D9 | 900x2300 | ALUMINIUM GLAZED DOOR | 01 | W9 | 1150X2300 | -DO- | 01 |
| D10 | 750x2000 | ALUMINIUM GLAZED DOUBLE SASHES DOOR | 01 | W10 | 2600X1500 | -DO- | 01 |
| | | | | | | | |
| F1 | 450x750 | ALUMINUM GLAZED FANLIGHT | 02 | | | | |
| F2 | 450x1200 | -DO- | 04 | | | | |
| F3 | 1100x750 | -DO- | 04 | | | | |
| F4 | 2050x600 | -DO- | 04 | | | | |

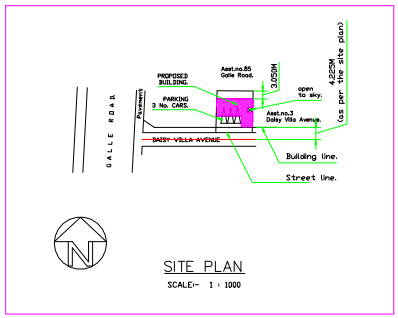


SITE PLAN

SCALE:- 1 : 1000

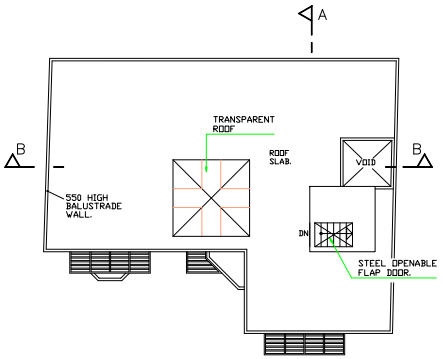


SITE PLAN

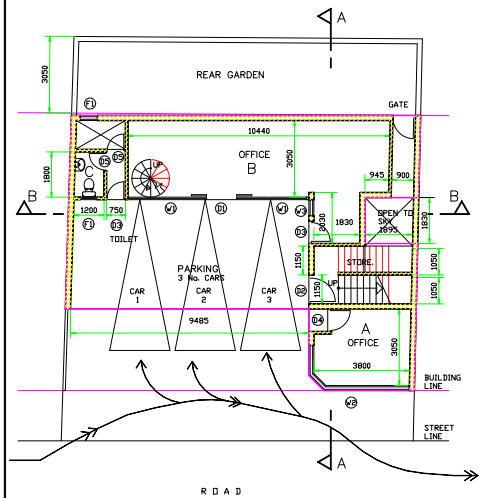


GROUND FLOOR PLAN

SCALE:- 1 : 1000

AREA :- 116.818 Sq.M.
(1257.419 Sq.ft)

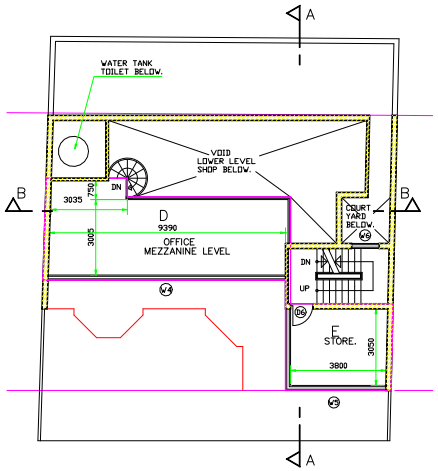


MEZZANINE FLOOR PLAN

AREA :- 49.572 Sq.M.
(533.588 Sq.ft)

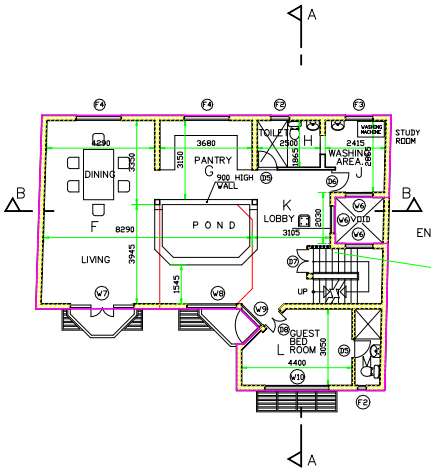


FIRST FLOOR PLAN

AREA :- 121.768 Sq.M.
(1310.700 Sq.ft)

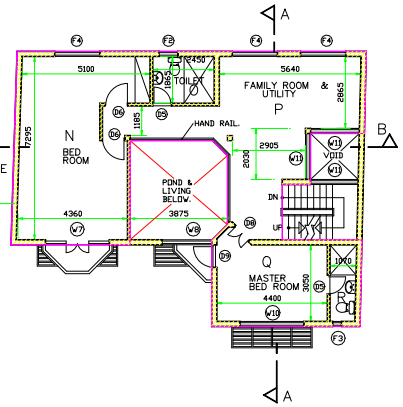


SECOND FLOOR PLAN

AREA :- 99.547 Sq.M.
(1071.515 Sq.ft)

PROPOSED FLAT AND OFFICE BUILDING

Notes :

AREA:-
OFFICES:
GF. 75.243 Sq.M.
MEZZ. 49.592 Sq.M. 116.410 Sq.M.

FLAT:
FIRST. 121.768 Sq.M.
SECOND 99.5147 Sq.M. 221.283 Sq.M.
TOTAL : 337.693 Sq.M.

APPLICANT'S SIGNATURE

DATE

TEAM FOUR
ARCHITECTS & ENGINEERS

Title :
COUNCIL DRAWING

SCALE : 1:100, 1:1000

DRAWN : Rn

AUGUST 2000

Architect:

DRG. No: T4/05/99/JD/A-01

REV.